




SECOND FLOOR LAYOUT(RHS) - SOUTH WING

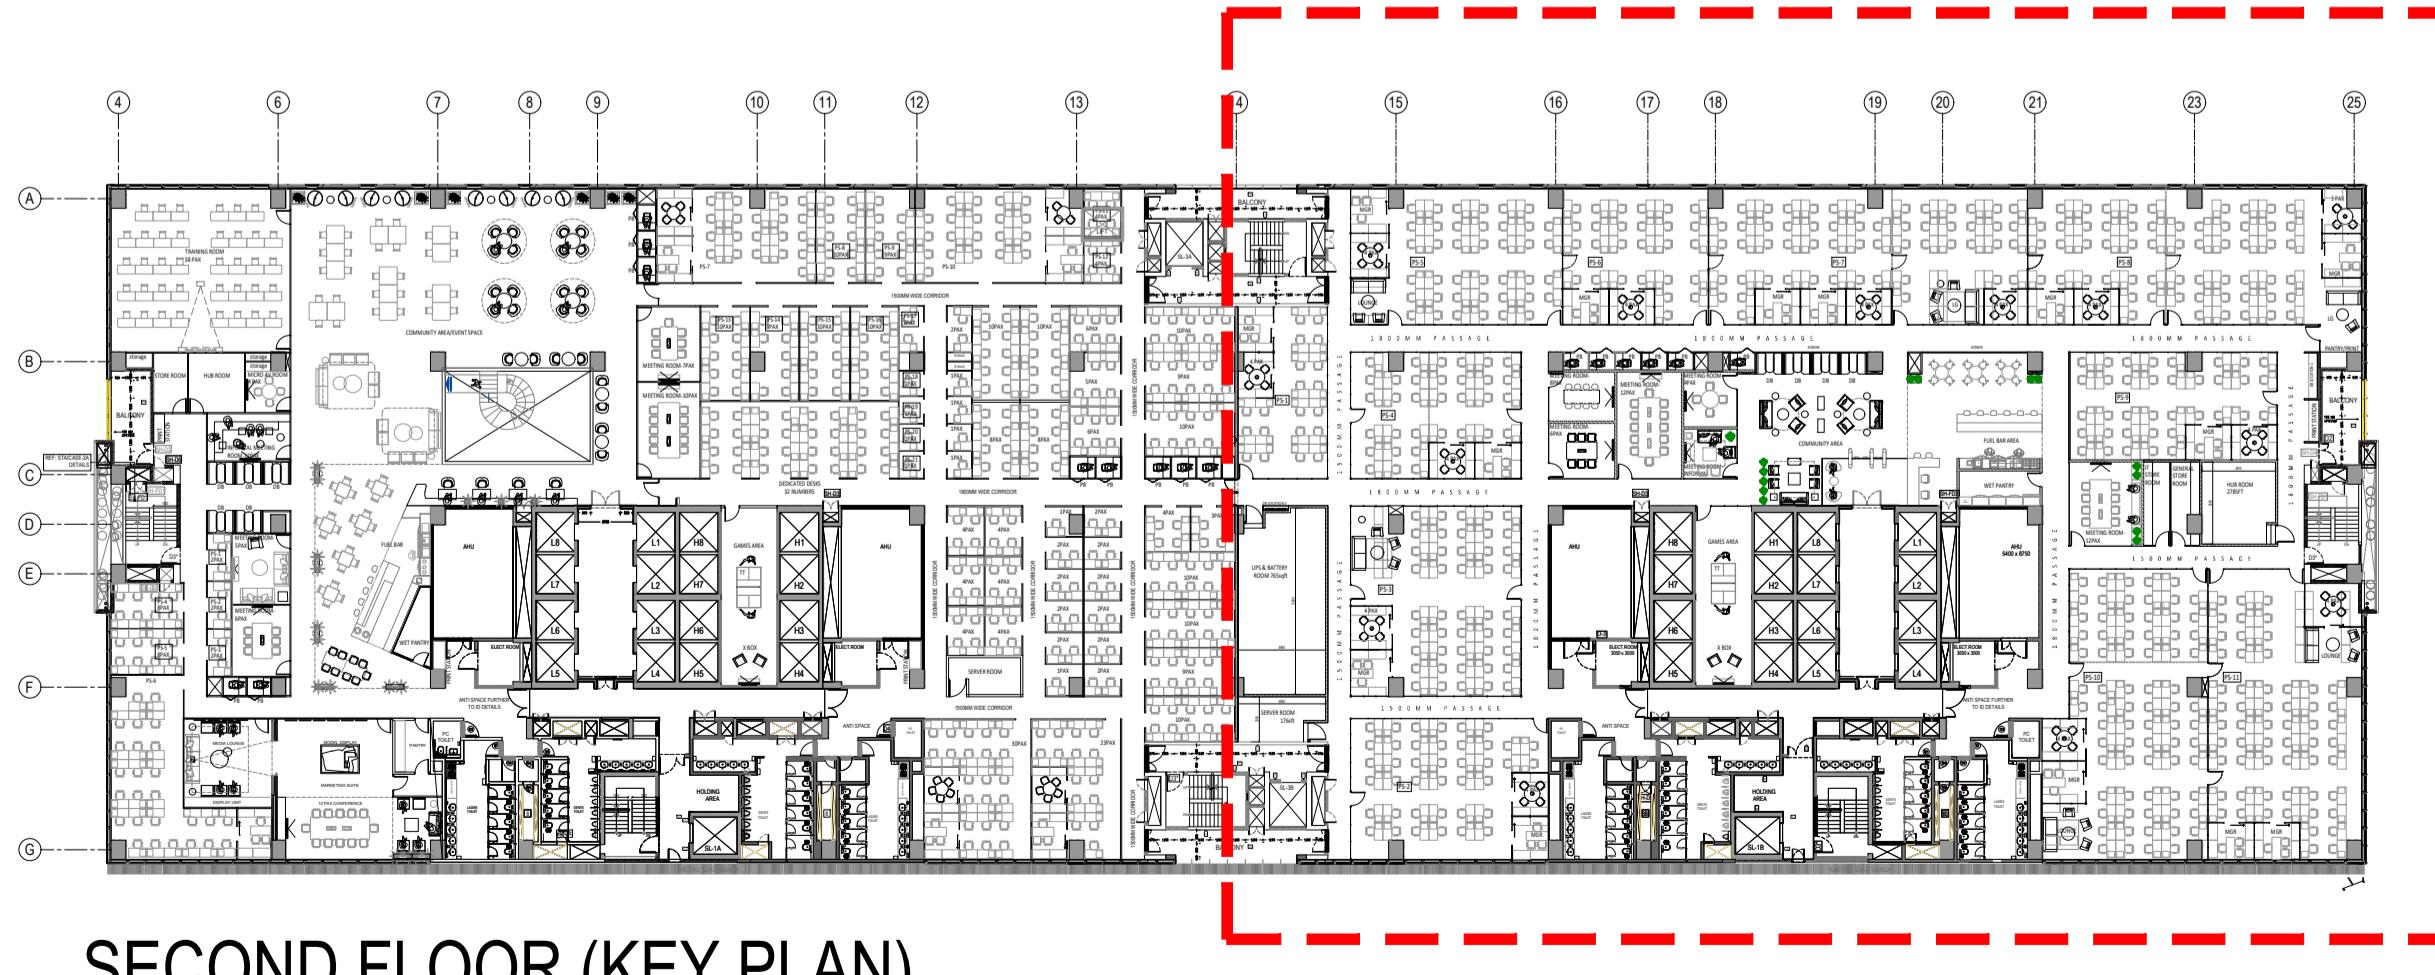


SECOND FLOOR (KEY PLAN)

OCCUPANCY CHART - HYD:SKYVIEW (SECOND FLOOR:RHS)

CARPET AREA FOR ZONE 2 - 32021.5SFT

SR.NO.	DESCRIPTION	QTY.	ACTUAL SEATS	CHARGEABLE SEATS
	PRIVATE OFFICE SEATS			
1	PS-1	1	21	27
2	PS-2	1	40	48
3	PS-3	1	46	59
4	PS-4	1	34	41
5	PS-5	1	41	52
6	PS-6	1	28	35
7	PS-7	1	56	80
8	PS-8	1	61	76
9	PS-9	1	37	44
10	PS-10	1	75	86
11	PS-11	1	60	78
	TOTAL HEADCOUNT		499	626
	FUEL BAR			
12	DINING SEATS			24
13	FUEL BAR SEATS			6
	TOTAL FUEL BAR SEATS			30
	ACTIVITY BASED SEATS - MEETING ROOMS			
14	INFORMAL MEETING ROOM	1		5
15	4 PAX MEETING ROOM	1		4
16	6 PAX MEETING ROOM	1		6
17	8 PAX MEETING ROOM	1		8
18	12 PAX MEETING ROOM	2		24
19	DISCUSSION BOOTHS	4		16
20	PHONE BOOTHS	6		6
	TOTAL			69

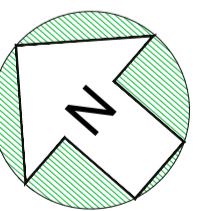

PROJECT TITLE COWRKS @ SKYVIEW

DRAWING TITLE
TURNITURE LAYOUT
SECOND FLOOR-SOUTH WING

CALE TS	DATE 17.10.18	DESIGNED SONIA	DRAWN SONIA
AGE	CONTRACT -	CHECKED PSN	APPROVED TEJ
DB NO.	DRAWING NO. <u>VIEW_SK_001_GF</u> SK_CW_201_2F		REV. R0
<p>THIS DRAWING IS THE PROPERTY OF DP ARCHITECTS PTE LTD NO PART OF THE DRAWING MAY BE REPRODUCED IN ANY MANNER WHATSOEVER WITHOUT PERMISSION FROM DP ARCHITECTS PTE LTD</p>			

NO PART OF THE DRAWING MAY BE REPRODUCED IN ANY MANNER
WHATSOEVER WITHOUT PERMISSION FROM DP ARCHITECTS PTE LTD

GEC DRAWING

GFC DRAWING