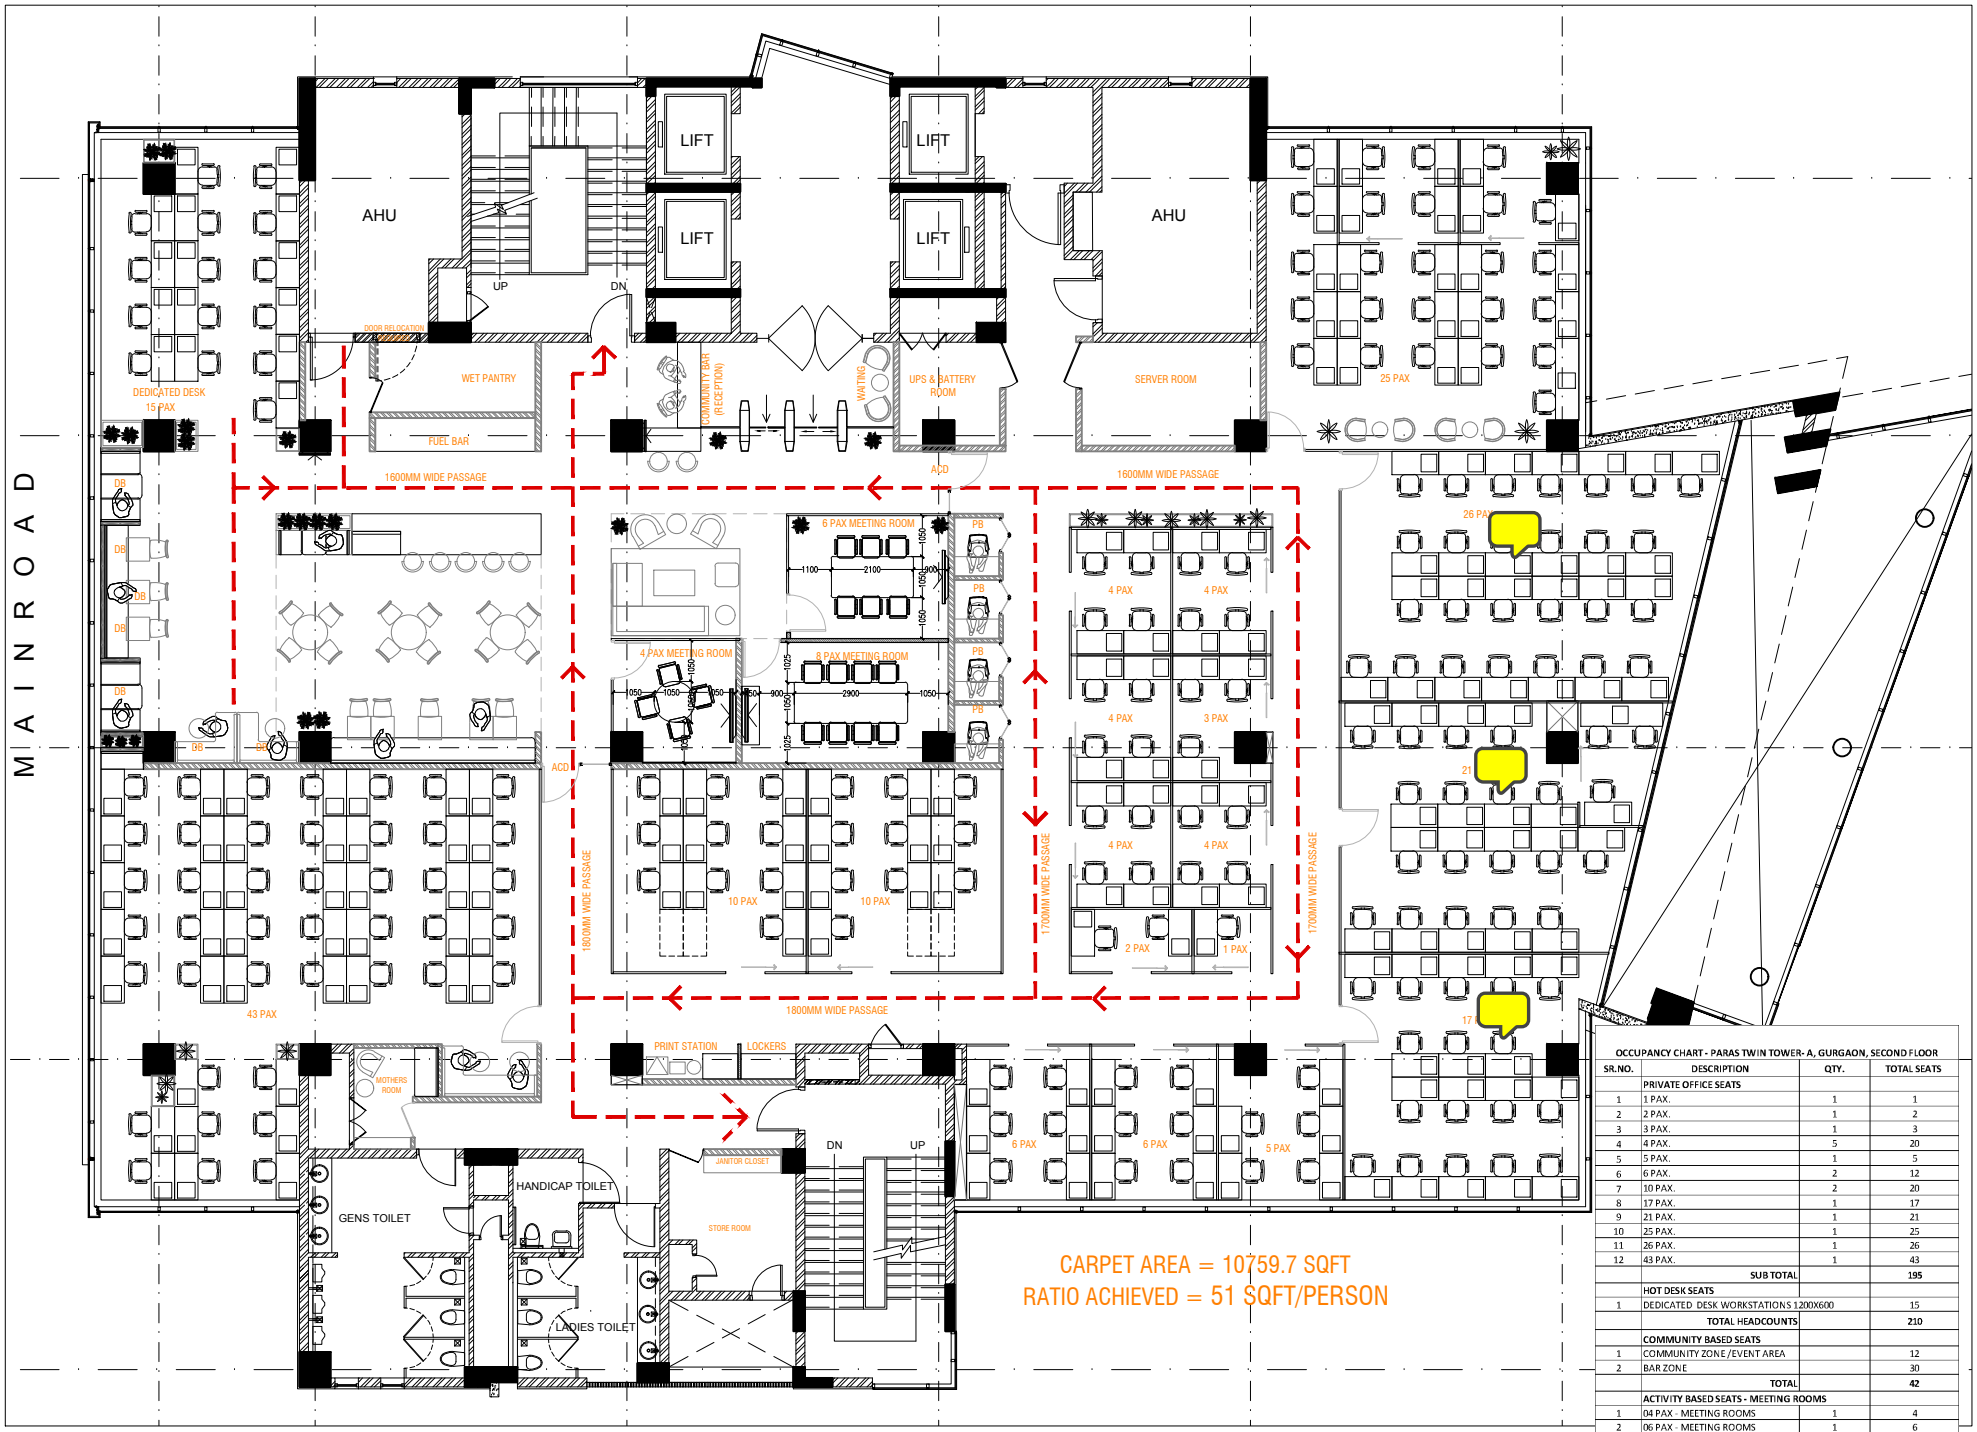

OCCUPANCY CHART - PARAS TWIN TOWER- A, GURGAON, SECOND FLOOR

SR.NO.	DESCRIPTION	QTY.	TOTAL SEATS
	PRIVATE OFFICE SEATS		
1	1 PAX.	1	1
2	2 PAX.	1	2
3	3 PAX.	1	3
4	4 PAX.	5	20
5	5 PAX.	1	5
6	6 PAX.	2	12
7	10 PAX.	2	20
8	17 PAX.	1	17
9	21 PAX.	1	21
10	25 PAX.	1	25
11	26 PAX.	1	26
12	43 PAX.	1	43
	SUB TOTAL		**195**
	HOT DESK SEATS		
1	DEDICATED DESK WORKSTATIONS 1200X600		15
	TOTAL HEADCOUNTS		**210**
	COMMUNITY BASED SEATS		
1	COMMUNITY ZONE /EVENT AREA		12
2	BAR ZONE		30
	TOTAL		**42**
	ACTIVITY BASED SEATS - MEETING ROOMS		
1	04 PAX - MEETING ROOMS	1	4
2	06 PAX - MEETING ROOMS	1	6
3	08 PAX - MEETING ROOMS	1	8
4	DISCUSSION BOOTHS	7	14
5	PHONE BOOTHS	4	4
	TOTAL		**36**

NOTES :

REVISIONS

DESCRIPTION	REV	APD	DATE

GENERAL NOTES

1. ALL DIMENSIONS ARE IN MILLIMETRES UNLESS OTHERWISE MENTIONED.
2. ONLY REFER TO PROVIDED DIMENSIONS AND DO NOT REPRODUCE OR SCALE THE DRAWINGS.
3. ALL SPOT LEVELS OR ELEVATION LEVELS MENTIONED IN THE DRAWING ARE ARCHITECTURAL FINISHED LEVELS, UNLESS MENTIONED OTHERWISE.
4. THE CIVIL CONTRACTOR SHALL CHECK AND VERIFY ALL DIMENSIONS AND LEVELS AND IMMEDIATELY REPORT TO ARCHITECT/PROJECT MANAGER ANY DISCREPANCIES FOUND BETWEEN ACTUAL FIELD CONDITIONS AND CONSTRUCTION DRAWINGS AND SHALL NOT PROCEED WITHOUT CLARIFYING THE SAME.
5. ALL ELEVATIONS ARE IN REFERENCE TO BENCHMARK AND THIS MUST BE VERIFIED BY THE CIVIL CONTRACTOR PRIOR TO GROUND BREAKING/EXCAVATION.
6. THIS DRAWING IS TO BE READ IN CONJUNCTION WITH RELEVENT STRUCTURAL AND SERVICE ENGINEER'S DRAWINGS.
7. THE CONTRACTOR SHALL IMMEDIATELY REPORT TO ARCHITECT/PROJECT MANAGER ANY DISCREPANCIES FOUND BETWEEN ARCHITECTURAL CONSTRUCTION DRAWINGS AND STRUCTURAL /SERVICE ENGINEER'S DRAWINGS AND SHALL NOT PROCEED WITHOUT CLARIFYING THE SAME.
8. THIS DRAWING TO BE READ WITH RELEVANT SERVICE ENGINEER'S DRAWINGS.
9. PLEASE REFER TO FINISHES SCHEDULE FOR ALL ARCHITECTURAL FINISHES.
10. THIS DOCUMENT, TOGETHER WITH THE CONCEPTS AND DESIGNS PRESENTED HERE IN, AS AN INSTRUMENT OF SERVICES, IS INTENDED ONLY FOR THE SPECIFIC PURPOSE AND CLIENT FOR WHICH IT WAS PREPARED. ANY OTHER USE OR DISTRIBUTION OF THIS DOCUMENT WHATSOEVER WITHOUT PRIOR WRITTEN AUTHORIZATION AND ADAPTATION BY DPE ARCHITECTS PTE LTD SHALL BE WITHOUT LIABILITY TO DPE ARCHITECTS PTE LTD.

DEVELOPER / LANDOWNER :

PARAS TWIN TOWER

PARAS BUILDTECH PVT. LTD, TOWER-A,
DLF GOLF COURSE RD, SECTOR 54,
GURUGRAM, HARYANA 122011

PHE, FIRE, HVAC & ELECTRICAL CONSULTANTS :

KEY PLAN

NORTH

PROJECT TITLE

COWRKS
PARAS TWIN TOWERS,
TOWER-A GURGAON

DRAWING TITLE

FURNITURE LAYOUT
SECOND FLOOR

SCALE	DATE	DESIGNED	DRAWN
1:100	29.10.18	PDY	PDY
STAGE	CONTRACT	CHECKED	APPROVED
-	-	PSN	TEJ

JOB NO.	DRAWING NO.	REV.
IN11A.A31.012	PARAS_CW_GF_001	

THIS DRAWING IS THE PROPERTY OF DP ARCHITECTS PTE LTD
NO PART OF THE DRAWING MAY BE REPRODUCED IN ANY MANNER WHATSOEVER WITHOUT PERMISSION FROM DP ARCHITECTS PTE LTD

FOR APPROVAL