


NOTES:			
REVISIONS			
DESCRIPTION	REV	APD	DATE
GENERAL NOTES			
1. ALL DIMENSIONS ARE IN MILLIMETERS UNLESS OTHERWISE MENTIONED. 2. REFER TO PROVIDED DIMENSIONS AND DO NOT REPRODUCE OR SCALE THE DRAWINGS. 3. ALL DIMENSIONS AND ELEVATIONS MENTIONED IN THE DRAWING ARE ARCHITECTURAL FINISHED LEVELS, UNLESS OTHERWISE STATED. 4. THE CIVIL CONTRACTOR SHALL CHECK AND VERIFY ALL DIMENSIONS AND LEVELS IMMEDIATELY AFTER RECEIVING THE DRAWINGS AND REPORT ANY DISCREPANCIES FOUND BETWEEN ACTUAL FIELD CONDITIONS AND CONSTRUCTION DRAWINGS AND SHALL NOT PROCEED WITH CONSTRUCTION UNTIL THESE ARE RESOLVED. 5. ALL ELEVATIONS ARE IN REFERENCE TO BRANCHMARKS AND THIS MUST BE VERIFIED BY THE CONTRACTOR PRIOR TO COMMENCING WORK. 6. BREAKING/EXCAVATION WORK IS TO BE CONDUCTED IN CONJUNCTION WITH RELEVANT STRUCTURAL AND SERVICE ENGINEER'S DRAWINGS. 7. THE CONTRACTOR IS ADVISED TO CONSULT THE CIVIL CONTRACTOR OR ARCHITECT/PROJECT MANAGER ANY DISCREPANCIES FOUND BETWEEN FIELD CONDITIONS AND CONSTRUCTION DRAWINGS AND SHALL NOT PROCEED WITHOUT CLARIFYING THE SAME. 8. PROCEDURES FOR CONSTRUCTION ARE TO BE IN ACCORDANCE WITH RELEVANT SERVICE ENGINEER'S DRAWINGS. 9. REFER TO THE SPECIFICATIONS FOR ALL ARCHITECTURAL FINISHES. 10. THIS DOCUMENT, TOGETHER WITH THE CONCEPTS AND DESIGNS PRESENTED HEREIN AS AN INSTRUMENT OF SERVICES, IS INTENDED ONLY FOR THE USE OF THE CONTRACTOR AND IS NOT TO BE COPIED OR REPRODUCED. USE OF AND IMPROPER RELIANCE ON THIS DOCUMENT WITHOUT THE WRITTEN APPROVAL AND ADAPTION BY DPE ARCHITECTS PTE LTD SHALL BE WITHOUT LIABILITY TO DPE ARCHITECTS PTE LTD.			
DEVELOPER / LANDOWNER	PURAVANKARA LTD	DESIGN EXECUTION	
COWRKS			
PH.E, FIRE, HVAC & ELECTRICAL CONSULTANTS			
KEY PLAN			
NORTH			
PROJECT TITLE	PURVA PREMIERE RESIDENCY ROAD BENGALURU		
DRAWING TITLE	FURNITURE LAYOUT FIRST FLOOR.		
SCALE	DATE	DESIGNED	DRAWN
1:150	22.09.18	RATI	VB
STAGE	CONTRACT	CHECKED	APPROVED
-	PSN	TEJ	
JOB NO	DRAWING NO.	REV.	
PP_CW_1F_001			RO
THIS DRAWING IS THE PROPERTY OF COWRKS NO PART OF THE DRAWING MAY BE REPRODUCED IN ANY MANNER WHATSOEVER WITHOUT PERMISSION FROM COWRKS			
GOOD FOR CONSTRUCTION			

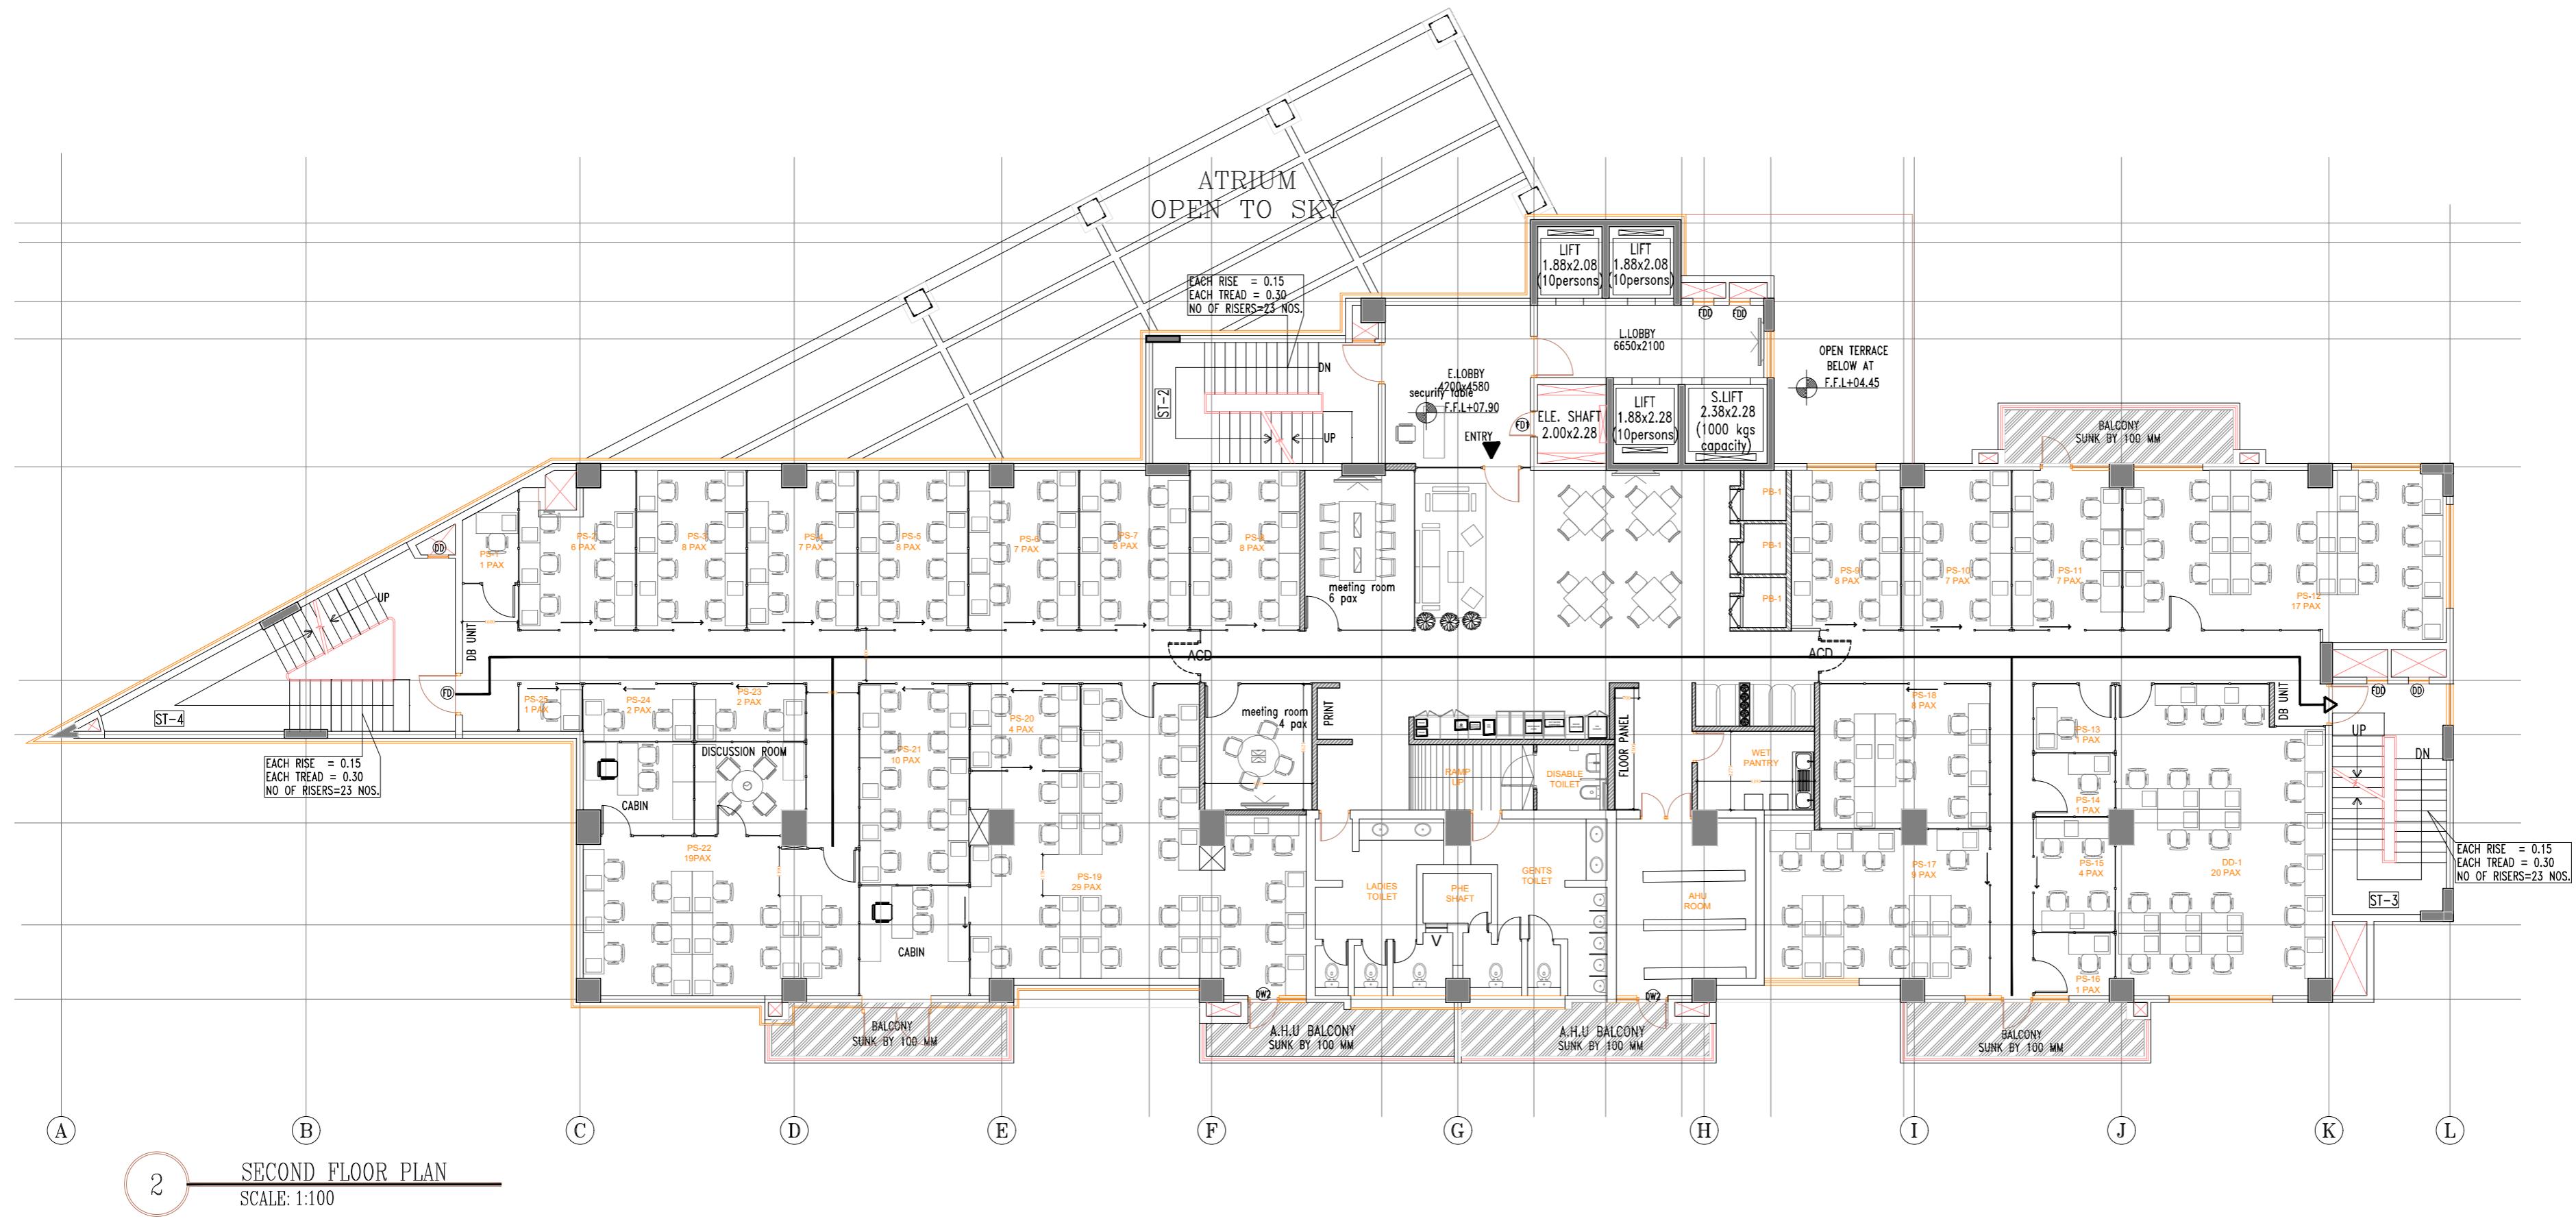


1. ALL DIMENSIONS ARE IN MILLIMETRES UNLESS OTHERWISE MENTIONED.
2. ONLY REFER TO PROVIDED DIMENSIONS AND DO NOT REPRODUCE OR SCALE THE DRAWINGS.
3. REFER TO SPOT LEVELS OR ELEVATION LEVELS MENTIONED IN THE DRAWINGS AS ARCHITECTURAL FINISHED LEVELS, UNLESS OTHERWISE MENTIONED.
4. THE CIVIL CONTRACTOR SHALL CHECK AND VERIFY ALL DIMENSIONS AND LEVELS AND IMMEDIATELY REPORT TO ARCHITECT/PROJECT MANAGER ANY DISCREPANCIES FOUND BETWEEN ACTUAL FIELD CONDITIONS AND CONSTRUCTION DRAWINGS AND SHALL NOT PROCEED WITH WORK UNTIL CLARIFYING THE SAME.
5. ALL ELEVATIONS ARE IN REFERENCE TO BENCHMARK AND THIS MUST BE VERIFIED BY THE CIVIL CONTRACTOR PRIOR TO GROUND BREAKING/EXCAVATION.
6. THIS DRAWING IS TO BE READ IN CONJUNCTION WITH RELEVANT STRUCTURAL AND SERVICE ENGINEER'S DRAWINGS.
7. THE CONTRACTOR SHALL IMMEDIATELY REPORT TO ARCHITECT/PROJECT MANAGER ANY DISCREPANCIES FOUND BETWEEN ARCHITECTURAL CONSTRUCTION DRAWINGS AND STRUCTURAL/SERVICE ENGINEER'S DRAWINGS AND SHALL NOT PROCEED WITHOUT CLARIFYING THE SAME.
8. SHAFT ENCLOSURES TO BE READ WITH RELEVANT SERVICE ENGINEER'S DRAWINGS
9. PLEASE REFER TO FINISHES SCHEDULE FOR ALL ARCHITECTURAL FINISHES.
10. THIS DOCUMENT, TOGETHER WITH THE CONCEPTS AND DESIGNS PRESENTED HEREIN, IS AN INSTRUMENT OF SERVICES, IS INTENDED ONLY FOR THE USE OF THE CONTRACTOR AND IS NOT TO BE COPIED, REPRODUCED, RESOLD OR IMPROPER RELIANCE ON THIS DOCUMENT WITHOUT PRIOR WRITTEN AUTHORIZATION AND ADAPTION BY DPE ARCHITECTS PTE LTD SHALL BE WITHOUT LIABILITY TO DPE ARCHITECTS PTE LTD.

DEVELOPER / LANDOWNER :
PURAVANKARA LTD
DESIGN EXECUTION
COWRKS
PHE, FIRE, HVAC & ELECTRICAL CONSULTANTS :

A large, blank rectangular area intended for a key plan or map.


PROJECT TITLE			
COWRKS			
PURVA PREMIERE			
RESIDENCY ROAD BENGALURU			
DRAWING TITLE			
FURNITURE LAYOUT SECOND FLOOR.			
SCALE	DATE	DESIGNED	DRAWN
1:150	22.09.18	RATI	VB
STAGE	CONTRACT	CHECKED	APPROVED
	-	PSN	TEJ
JOB NO.	DRAWING NO.		REV.
	PP_CW_2F_001		R0
THIS DRAWING IS THE PROPERTY OF COWRKS NO PART OF THE DRAWING MAY BE REPRODUCED IN ANY MANNER WHATSOEVER WITHOUT PERMISSION FROM COWRKS			
GOOD FOR CONSTRUCTION			

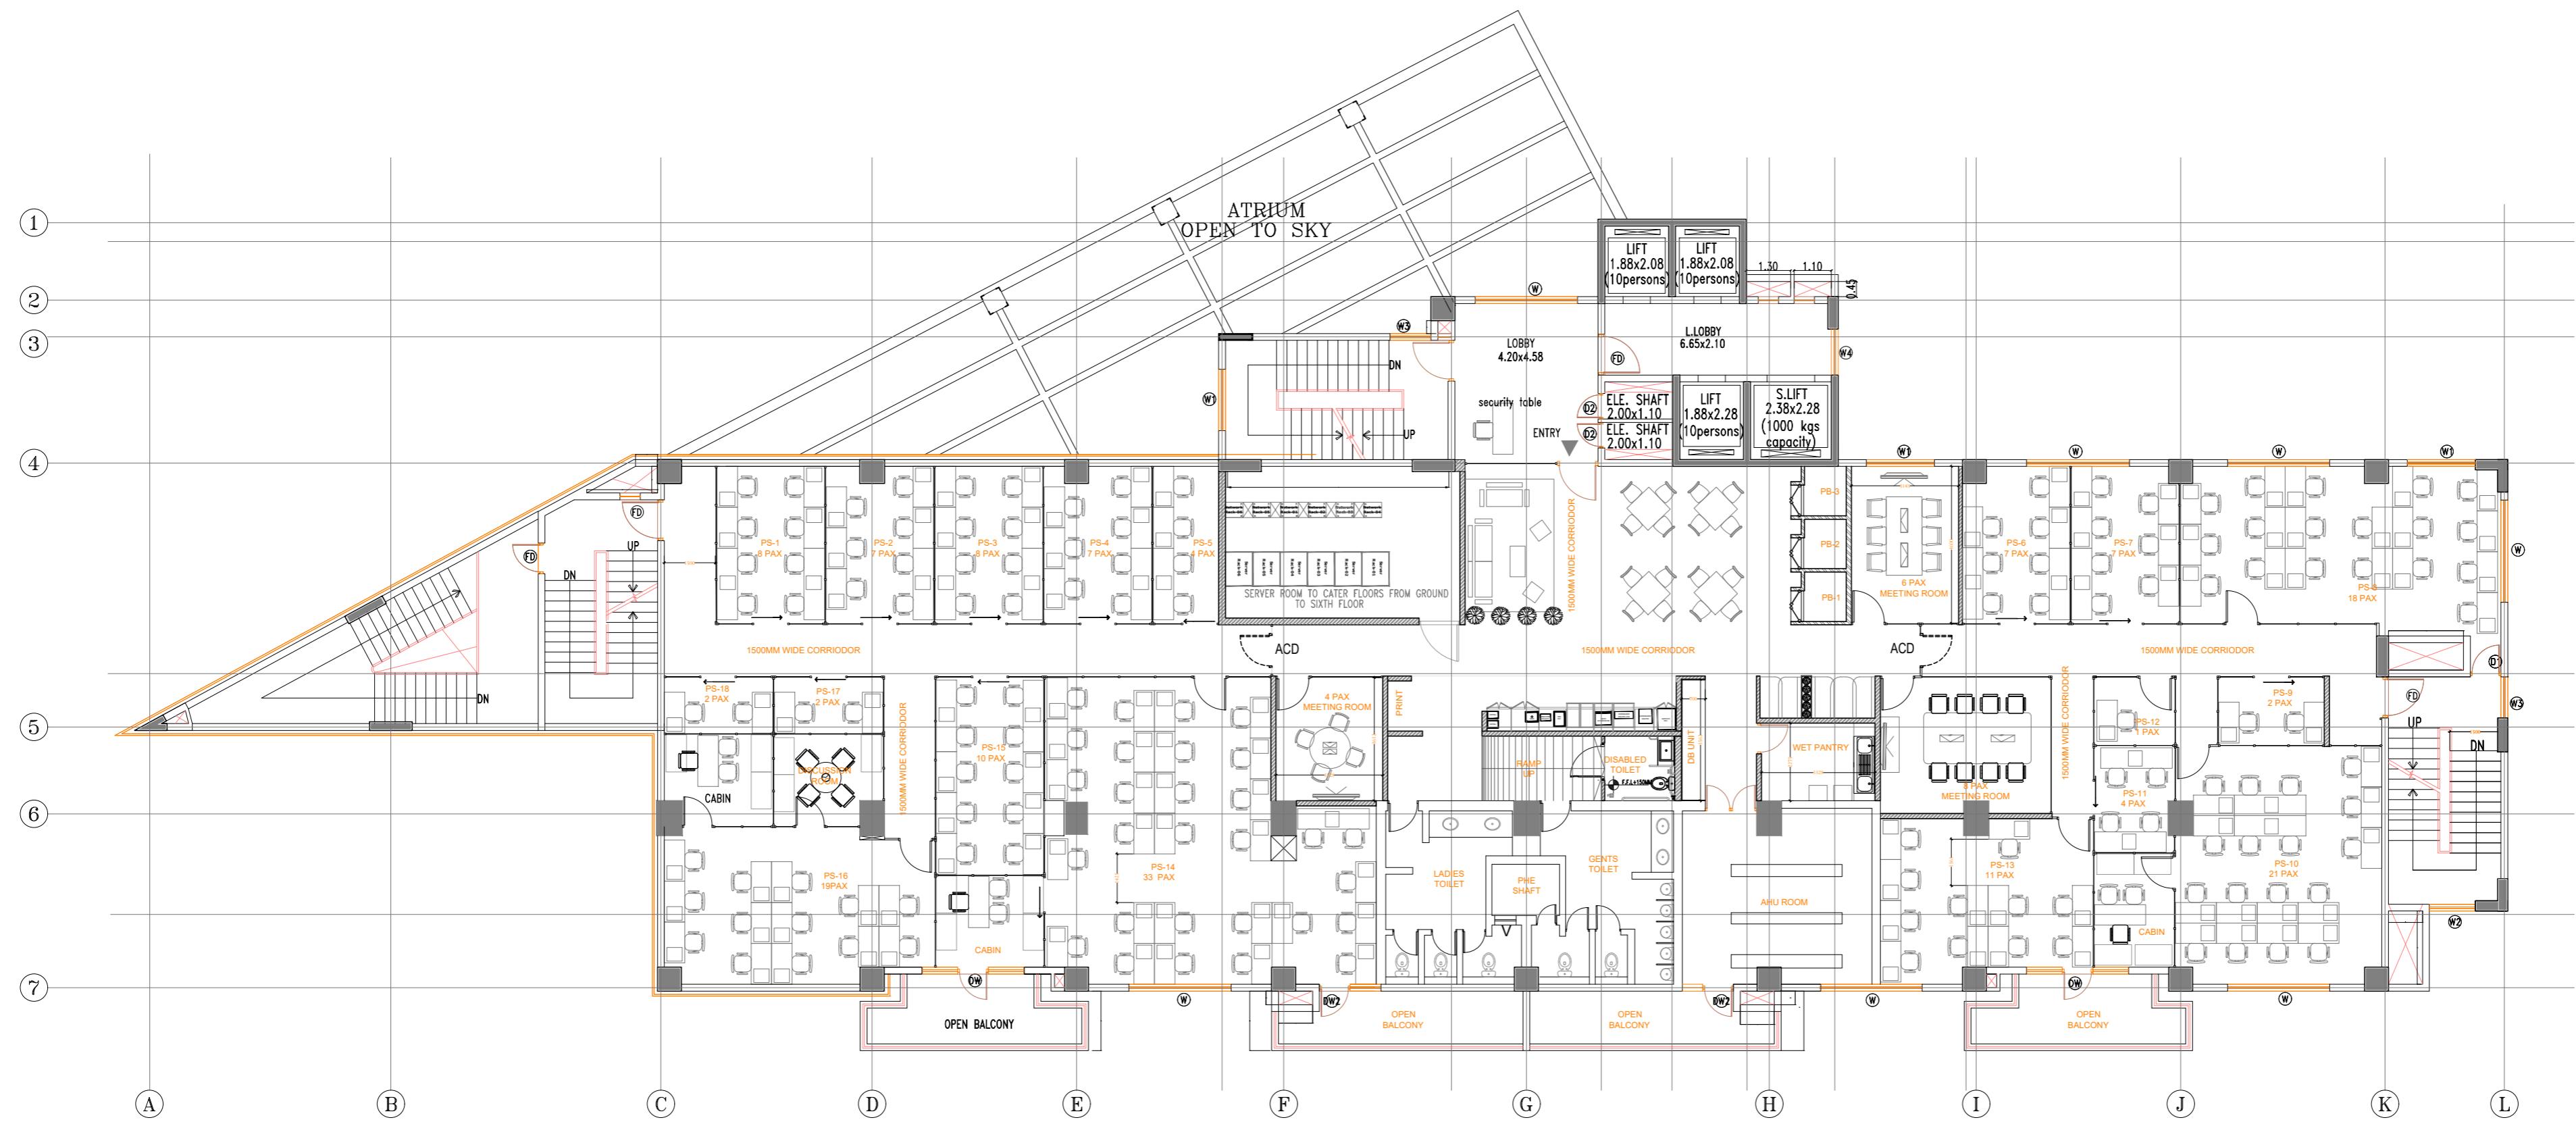

1 THIRD FLOOR PLAN

SCALE: 1:100

KEY PLAN			
NORTH		PROJECT TITLE	COWRKS PURVA PREMIERE RESIDENCY ROAD BENGALURU
DRAWING TITLE			
FURNITURE LAYOUT THIRD FLOOR.			
SCALE	DATE	DESIGNED	DRAWN
1:150	22.09.18	RATI	VB
STAGE	CONTRACT	CHECKED	APPROVED
-		PSN	TEJ
JOB NO.	DRAWING NO.	REV.	
PP_CW_3F_301			
THIS DRAWING IS THE PROPERTY OF COWRKS NO PART OF THE DRAWING MAY BE REPRODUCED IN ANY MANNER WHATSOEVER WITHOUT PERMISSION FROM COWRKS			
GOOD FOR CONSTRUCTION			

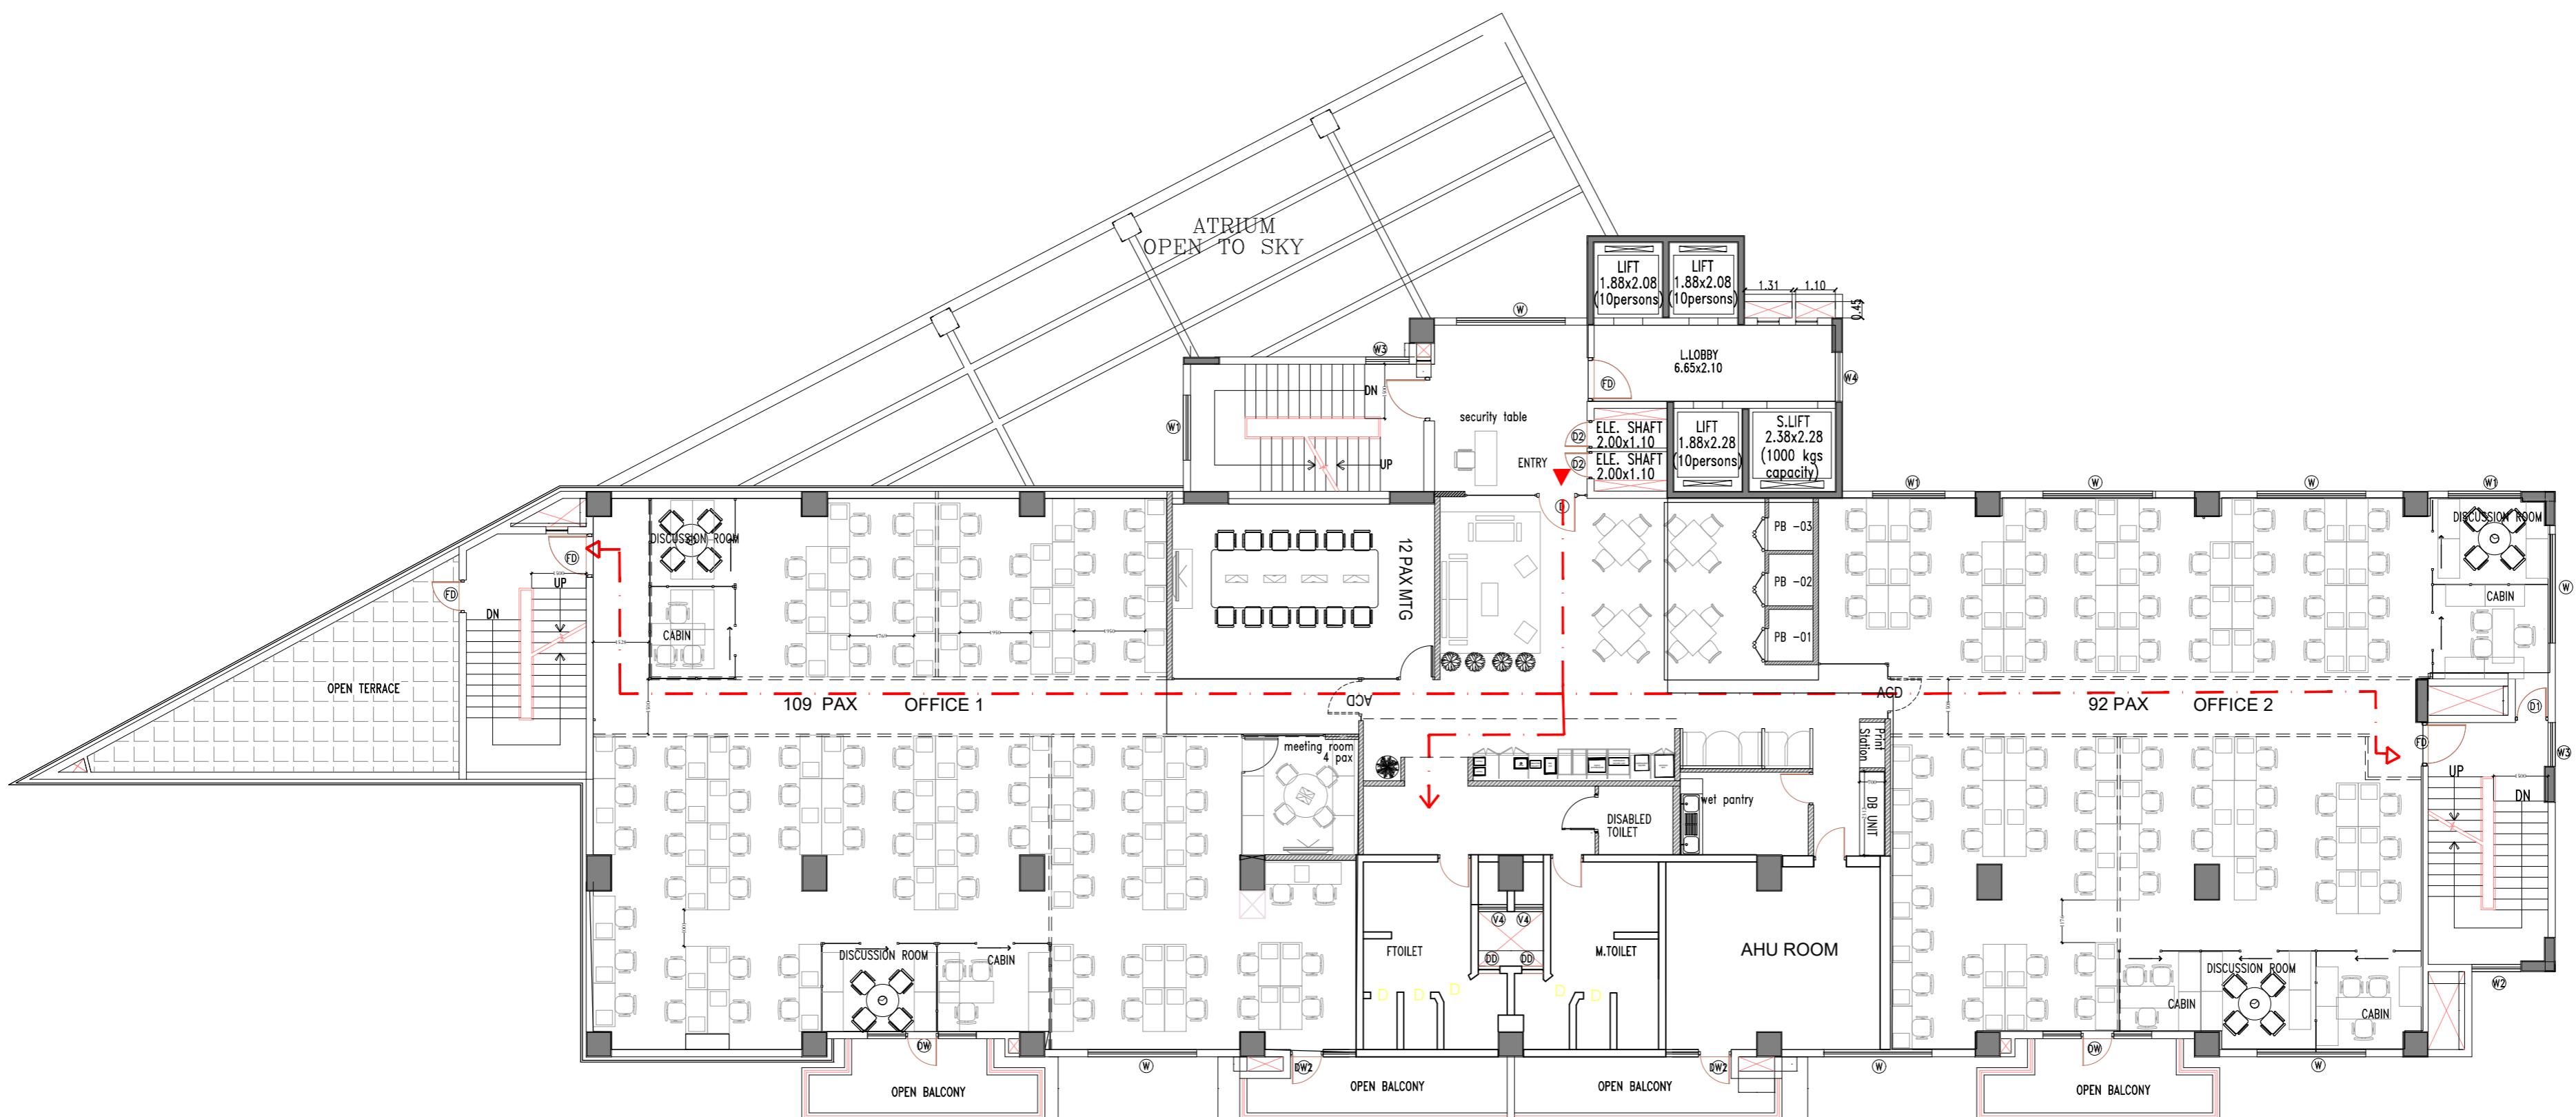

FOURTH FLOOR PLAN

SCALE: 1:100

1

NOTES:							
REVISIONS							
DESCRIPTION	REV	APD	DATE				
GENERAL NOTES							
1. ALL DIMENSIONS ARE IN MILLIMETRES UNLESS OTHERWISE MENTIONED. 2. DO NOT PROVIDE DIMENSIONS AND DO NOT REPRODUCE OR SCALE THE DRAWINGS. 3. REFER TO THE ELEVATION LEVELS MENTIONED IN THE DRAWING AS ARCHITECTURAL FINISHED LEVELS, UNLESS OTHERWISE MENTIONED. 4. CONTRACTOR SHALL CHECK AND VERIFY ALL DIMENSIONS AND LEVELS AND IMMEDIATELY REPORT TO ARCHITECT/PROJECT MANAGER IF ANY DISCREPANCIES ARE FOUND. THIS MUST BE DONE IN FIELD CONDITIONS AND CONSTRUCTION DRAWINGS AND SHALL NOT BE BASED ON PAPERWORK. THIS IS TO ENSURE THAT THE PROJECT IS CONSTRUCTED ACCORDING TO THE DRAWINGS. 5. ALL ELEVATIONS ARE REFERENCED TO BENCHMARK AND THIS MUST BE VERIFIED BY CONTRACTOR PRIOR TO COMMENCING BREAKING/EXCAVATION. 6. CONTRACTOR SHALL READ IN CONJUNCTION WITH RELEVANT STRUCTURAL AND SERVICE ENGINEER'S DRAWINGS. 7. CONTRACTOR SHALL NOT MAKE ANY CHANGES TO THE DRAWINGS WITHOUT APPROVAL OF THE ARCHITECT/PROJECT MANAGER. ANY DISCREPANCIES FOUND BETWEEN ARCHITECTURAL CONSTRUCTION DRAWINGS AND SITE SHALL NOT PROCEED WITHOUT CLARIFYING THE SAME WITH THE RELEVANT SERVICE ENGINEER'S DRAWINGS. 8. CONTRACTOR SHALL PREPARE A CHECKLIST FOR ALL ARCHITECTURAL FINISHES. 9. CONTRACTOR SHALL PREPARE A CHECKLIST FOR ALL ARCHITECTURAL FINISHES. 10. THIS DOCUMENT, TOGETHER WITH THE CONCEPTS AND DESIGNS PRESENTED HEREIN, AS AN INSTRUMENT OF SERVICES, IS INTENDED TO PREPARE, ISSUE OF AND IMPROPER RELIANCE ON THIS DOCUMENT IS PROHIBITED. THE CONTRACTOR SHALL NOT RELY ON THIS DOCUMENT. DPE ARCHITECTS PTE LTD SHALL BE WITHOUT LIABILITY TO DPE ARCHITECTS PTE LTD.							
DEVELOPER / LANDOWNER:	PURAVANKARA LTD						
DESIGN EXECUTION:	COWRKS						
PHE, FIRE, HVAC & ELECTRICAL CONSULTANTS :							
KEY PLAN							
NORTH							
PROJECT TITLE							
COWRKS PURVA PREMIERE RESIDENCY ROAD BENGALURU							
DRAWING TITLE							
FURNITURE LAYOUT FOURTH FLOOR.							
SCALE	DATE	DESIGNED	DRAWN				
1:150	22.09.18	RATI	VB				
STAGE	CONTRACT	CHECKED	APPROVED				
-	-	PSN	TEJ				
JOB NO.	DRAWING NO.	REV.					
PP_CW_4F_401	R0						
THIS DRAWING IS THE PROPERTY OF COWRKS NO PART OF THE DRAWING MAY BE REPRODUCED IN ANY MANNER WHATSOEVER WITHOUT PERMISSION FROM COWRKS							
GOOD FOR CONSTRUCTION							




1 5TH FLOOR
SCALE: 1:125

OCCUPANCY CHART - PURVA PREMIERE 5th FLOOR COWRKS+

SR.NO.	DESCRIPTION	QTY.	TOTAL SEATS ACHIEVABLE	TOTAL PROPOSED
PRIVATE OFFICE SEATS				
1	OFFICE 1- 34 PAX	1	34	26
2	OFFICE 2 - 69 PAX	1	69	61
3	OFFICE 3 - 42 PAX	1	42	38
4	OFFICE 4 - 52 PAX	1	52	42
SUB TOTAL			197	167
TOTAL HEADCOUNTS			197	167
COMMUNITY BASED SEATS				
1	COMMUNITY ZONE /EVENT AREA			
2	BAR ZONE			
ACTIVITY BASED SEATS - MEETING ROOMS				
1	12 PAX - MEETING ROOM-1	1	12	
2	4 PAX - MEETING ROOM-3	1	4	
1	PHONE BOOTHS	3	3	
2	DISCUSSION BOOTHS	1.5	3	
TOTAL			6	

NOTES:				
REVISIONS DESCRIPTION	REV	APD	DATE	
GENERAL NOTES				
1. ALL DIMENSIONS ARE IN MILLIMETERS UNLESS OTHERWISE MENTIONED. 2. NOT TO BE PROVIDED DIMENSIONS AND DO NOT REPRODUCE OR SCALE THE DRAWINGS. 3. ALL DIMENSIONS AND ELEVATIONS ON THIS DRAWING LEVELS MENTIONED IN THE DRAWING ARE ARCHITECTURAL FINISHED LEVELS, UNLESS OTHERWISE STATED. 4. THE CIVIL CONTRACTOR SHALL CHECK AND VERIFY ALL DIMENSIONS AND LEVELS AND IMMEDIATELY REPORT ANY DISCREPANCIES FOUND BETWEEN ACTUAL FIELD CONDITIONS AND CONSTRUCTION DRAWINGS AND SHALL NOT PROCEED WITH CONSTRUCTION UNTIL THESE ARE RESOLVED. 5. ALL ELEVATIONS ARE IN REFERENCE TO BRANCHMARKS AND THIS MUST BE VERIFIED BY THE CONTRACTOR PRIOR TO COMMENCING WORK. 6. BREAKING/CAVATION TO EXISTING STRUCTURE IS TO BE DONE IN CONJUNCTION WITH RELEVANT STRUCTURAL AND SERVICE ENGINEER'S DRAWINGS. 7. THE CONTRACTOR IS REQUESTED TO NOTIFY THE ARCHITECT/PROJECT MANAGER ANY DISCREPANCIES FOUND IN THE CONSTRUCTION DRAWINGS AND NOT TO PROCEED WITHOUT CONSULTATION WITH THE ARCHITECT/PROJECT MANAGER AND THE RELEVANT STRUCTURAL/SERVICE ENGINEER'S DRAWINGS AND SHALL NOT PROCEED WITHOUT CLARIFYING THE SAME. 8. THIS DOCUMENT, TOGETHER WITH THE CONCEPTS AND DESIGNS PRESENTED HEREIN AS AN INSTRUMENT OF SERVICES, IS INTENDED ONLY FOR THE USE OF THE CONTRACTOR AND IS NOT TO BE COPIED, REPRODUCED, OR ADAPTED IN WHOLE OR IN PART. ANY SUCH USE, COPIING, REPRODUCTION OR ADAPTATION BY DPE ARCHITECTS PTE LTD SHALL BE WITHOUT LIABILITY TO DPE ARCHITECTS PTE LTD.				
DEVELOPER / LANDOWNER	PURAVANKARA LTD			
DESIGN EXECUTION				
COWRKS				
PHE, FIRE, HVAC & ELECTRICAL CONSULTANTS				
KEY PLAN				
NORTH				
PROJECT TITLE	COWRKS PURVA PREMIERE RESIDENCY ROAD BENGALURU			
DRAWING TITLE	FURNITURE LAYOUT FIFTH FLOOR.			
SCALE	DATE	DESIGNED	DRAWN	
1:125	20.12.18	RATI	VB	
STAGE	CONTRACT	CHECKED	APPROVED	
	-	PSN	TEJ	
JOB NO	DRAWING NO.	REV.		
	PP_CW_5F_501			
THIS DRAWING IS THE PROPERTY OF COWRKS NO PART OF THE DRAWING CAN BE REPRODUCED IN ANY MANNER WHATSOEVER WITHOUT PERMISSION FROM COWRKS				
GOOD FOR CONSTRUCTION				

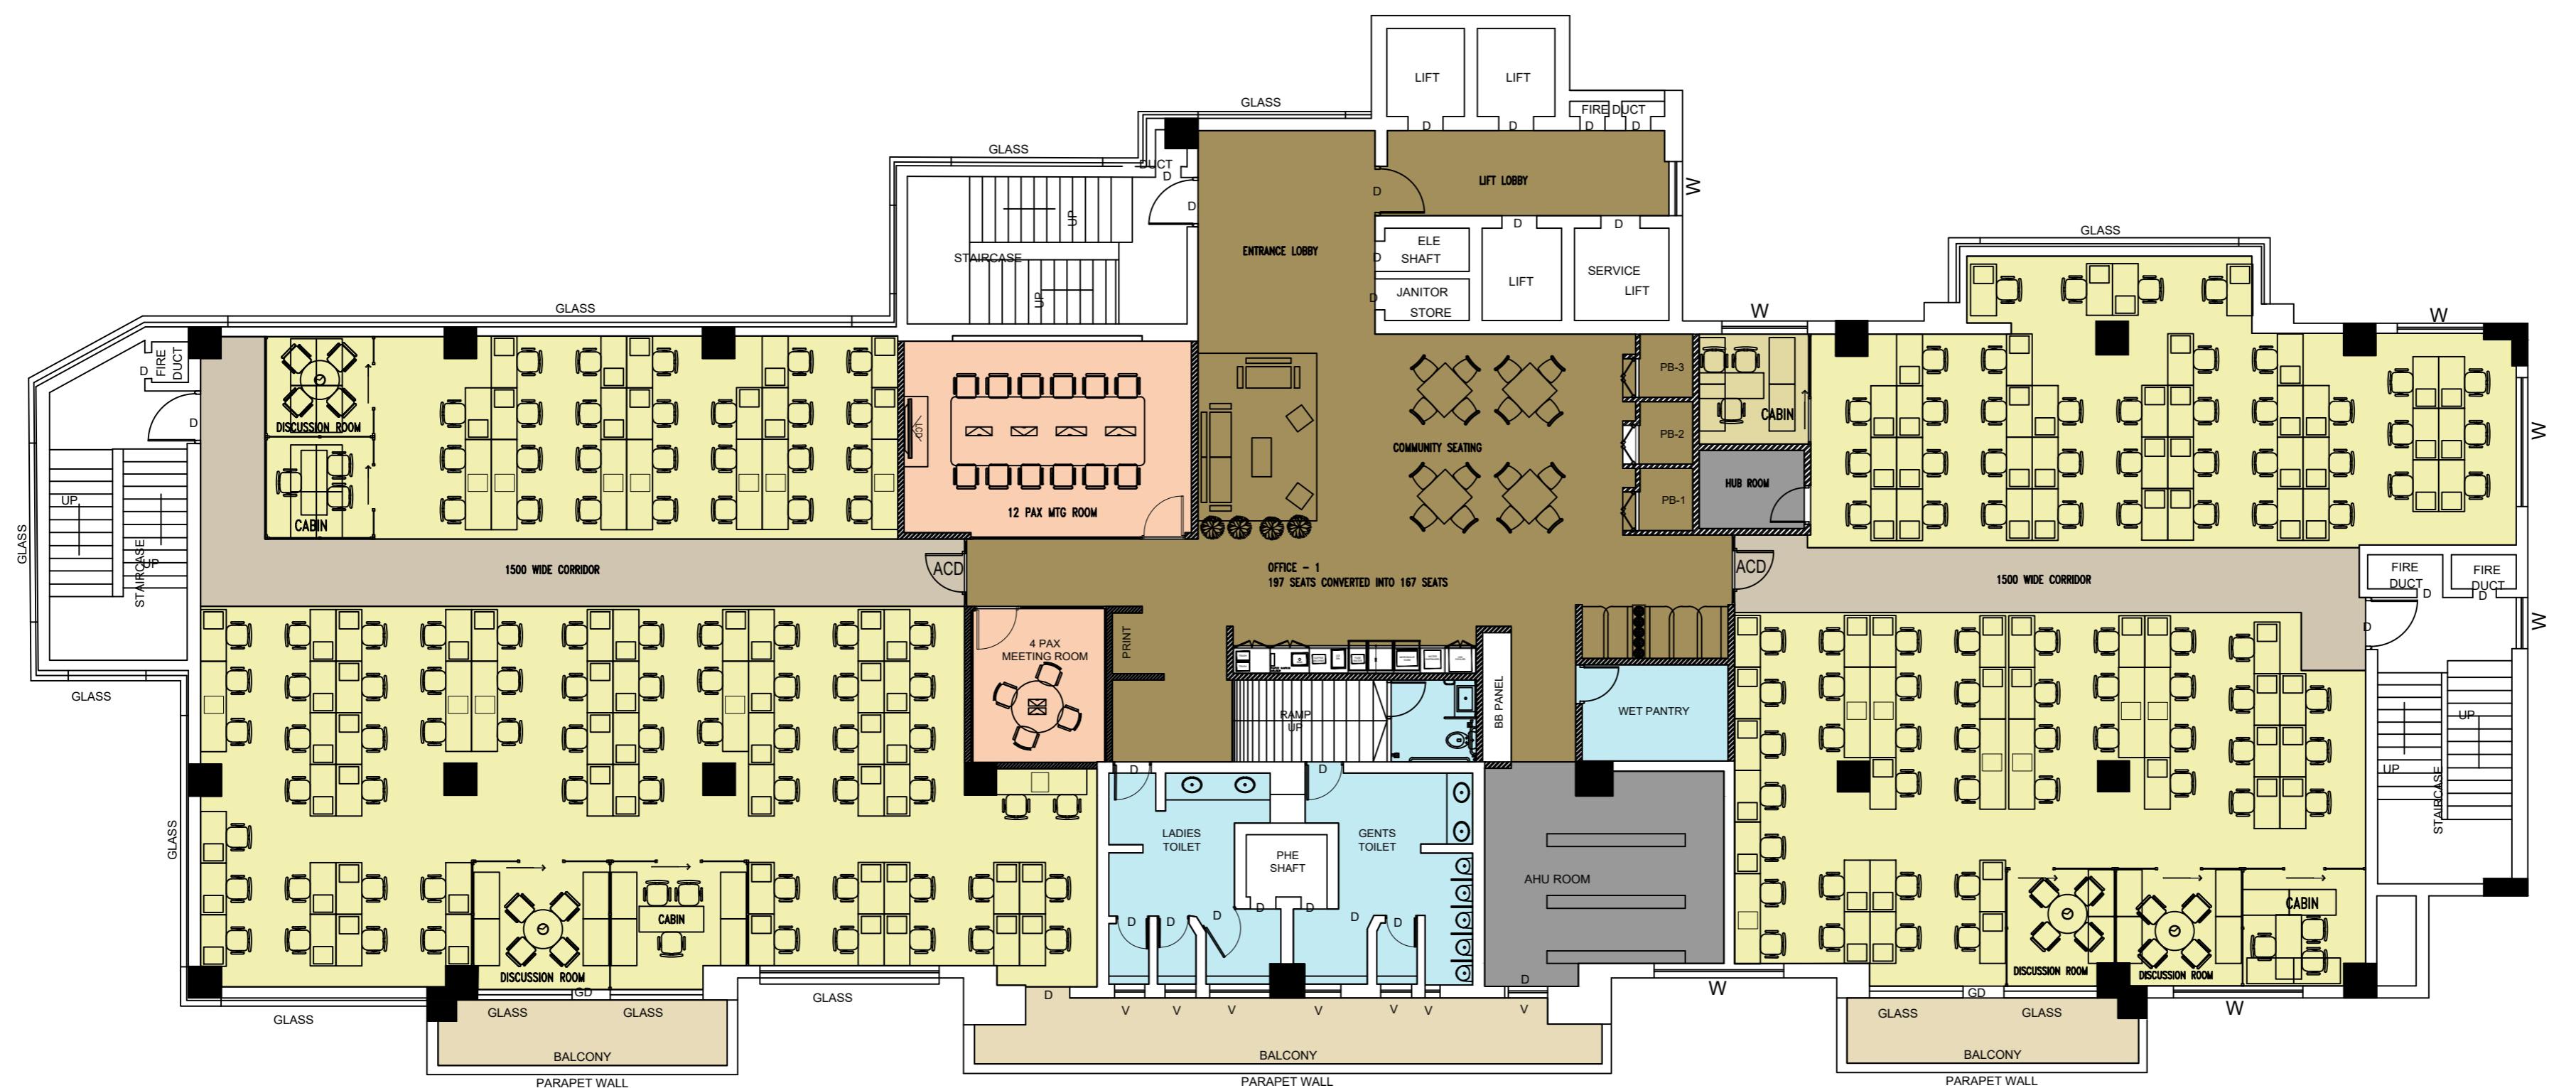

1 6TH TO 8TH FLOOR
SCALE: 1:125

OCCUPANCY CHART - PURVA PREMIERE 5th FLOOR COWRKS+				
S.R.NO.	DESCRIPTION	QTY.	TOTAL SEATS ACHIEVABLE	TOTAL PROPOSED
	PRIVATE OFFICE SEATS			
1	OFFICE 1- 197 PAX	1	197	167
	SUB TOTAL		197	167
	TOTAL HEADCOUNTS		197	167
	COMMUNITY BASED SEATS			
1	COMMUNITY ZONE /EVENT AREA			
2	BAR ZONE			
	ACTIVITY BASED SEATS - MEETING ROOMS			
1	12 PAX - MEETING ROOM-1	1	12	
2	4 PAX - MEETING ROOM-3	1	4	
1	PHONE BOOTHS	3	3	
2	DISCUSSION BOOTHS	1.5	3	
	TOTAL		6	

NOTES:				
REVISIONS	DESCRIPTION	REV	APD	DATE
GENERAL NOTES				
1. ALL DIMENSIONS ARE IN MILLIMETRES UNLESS OTHERWISE MENTIONED. 2. IT IS THE DUTY OF THE PROVIDER DIMENSIONS AND DO NOT REPRODUCE OR SCALE THE DRAWINGS. 3. THE DRAWINGS ARE FOR INFORMATION LEVELS MENTIONED IN THE DRAWING ARE ARCHITECTURAL FINISHED LEVELS, UNLESS OTHERWISE STATED. 4. THE CIVIL CONTRACTOR SHALL CHECK AND VERIFY ALL DIMENSIONS AND IMMEDIATELY REPORT ANY DISCREPANCIES FOUND BETWEEN ACTUAL FIELD CONDITIONS AND CONSTRUCTION DRAWINGS AND SHALL NOT PROCEED WITHOUT CLARIFYING THE SAME. 5. ALL ELEVATIONS ARE IN REFERENCE TO BENCHMARK AND THIS MUST BE MAINTAINED. 6. BREAKING/EXCAVATION TO BE MADE IN CONJUNCTION WITH RELEVANT STRUCTURAL AND SERVICE ENGINEER'S DRAWINGS. 7. THE CONTRACTOR SHALL NOTIFY THE ARCHITECT/PROJECT MANAGER ANY DISCREPANCIES FOUND IN THE CONSTRUCTION DRAWINGS AND SHALL NOT PROCEED WITHOUT CLARIFYING THE SAME. 8. PROCEDURES DRAWN BY THE CONTRACTOR SHALL BE IN ACCORDANCE WITH THE SAME. 9. THE CONTRACTOR SHALL MAINTAIN A CHECKLIST SCHEDULE FOR ALL ARCHITECTURAL FINISHES. 10. THIS DOCUMENT, TOGETHER WITH THE CONCEPTS AND DESIGNS PRESENTED HEREIN AS AN INSTRUMENT OF SERVICES, IS INTENDED ONLY FOR THE USE OF THE CONTRACTOR AND IS NOT TO BE COPIED OR REPRODUCED. USE OF AND IMPROPER RELIANCE ON THIS DOCUMENT WITHOUT THE WRITTEN APPROVAL AND ADVICE OF DPE ARCHITECTS PTE LTD SHALL BE WITHOUT LIABILITY TO DPE ARCHITECTS PTE LTD.				
DEVELOPER / LANDOWNER:	PURAVANKARA LTD			
DESIGN EXECUTION:	COWRKS			
PHE, FIRE, HVAC & ELECTRICAL CONSULTANTS:				
KEY PLAN				
NORTH				
PROJECT TITLE:	COWRKS PURVA PREMIERE RESIDENCY ROAD BENGALURU			
DRAWING TITLE:	FURNITURE LAYOUT 6TH TO 8TH FLOOR.			
SCALE	DATE	DESIGNED	DRAWN	
1:125	20.12.18	RATI	VB	
STAGE	CONTRACT	CHECKED	APPROVED	
-		PSN	TEJ	
JOB NO.	DRAWING NO.	REV.		
	PP_CW_6F_601			
THIS DRAWING IS THE PROPERTY OF COWRKS NO PART OF THE DRAWING MAY BE REPRODUCED IN ANY MANNER WHATSOEVER WITHOUT PERMISSION FROM COWRKS				
GOOD FOR CONSTRUCTION				



1 9TH FLOOR
SCALE: 1:125

OCCUPANCY CHART - PURVA PREMIERE 9th FLOOR COWRKS ENTERPRISE

SR.NO.	DESCRIPTION	QTY.	TOTAL SEATS ACHIEVABLE	TOTAL PROPOSED
PRIVATE OFFICE SEATS				
1	OFFICE 1- 34 PAX	1	161	145
	SUB TOTAL		161	145
	TOTAL HEADCOUNTS		161	145
COMMUNITY BASED SEATS				
1	COMMUNITY ZONE /EVENT AREA			
2	BAR ZONE			
ACTIVITY BASED SEATS - MEETING ROOMS				
1	12 PAX - MEETING ROOM-1	1	12	
1	PHONE BOOTHS	3	3	
2	DISCUSSION BOOTHS	1.5	3	
	TOTAL		6	

NOTES:			
REVISIONS DESCRIPTION	REV	APD	DATE
GENERAL NOTES			
1. ALL DIMENSIONS ARE IN MILLIMETRES UNLESS OTHERWISE MENTIONED. 2. REFER TO PROVIDED DIMENSIONS AND DO NOT REPRODUCE OR SCALE THE DRAWINGS. 3. ALL ELEVATIONS ARE IN RELATION TO ESTATE ELEVATION LEVELS MENTIONED IN THE DRAWING ARE ARCHITECTURAL FINISHED LEVELS, UNLESS OTHERWISE STATED. 4. THE CIVIL CONTRACTOR SHALL CHECK AND VERIFY ALL DIMENSIONS AND LEVELS AND REPORT ANY DISCREPANCIES TO THE ARCHITECT/PROJECT MANAGER. ANY DISCREPANCIES FOUND MUST BE CORRECTED IMMEDIATELY AND NO WORK SHOULD BE PROCEEDED UNTIL CORRECTION IS MADE. 5. ALL ELEVATIONS ARE IN REFERENCE TO BENCHMARK AND THIS MUST BE VERIFIED BY THE CONTRACTOR. 6. ALL EXCAVATION WORKS TO BE READ IN CONJUNCTION WITH RELEVANT STRUCTURAL AND SERVICE ENGINEER'S DRAWINGS. 7. THE CONTRACTOR SHALL NOT PROCEED WITH CONSTRUCTION UNTIL THE ARCHITECT/PROJECT MANAGER ANY DISCREPANCIES FOUND ARE CORRECTED AND NO WORK SHOULD BE PROCEEDED UNTIL CORRECTION IS MADE. 8. PROCEED WITHOUT CLARIFYING THE RELEVANT SERVICE ENGINEER'S DRAWINGS. 9. REFER TO SPECIFICATIONS SCHEDULE FOR ALL ARCHITECTURAL FINISHES. 10. THIS DOCUMENT, TOGETHER WITH THE CONCEPTS AND DESIGNS PRESENTED HEREIN AS AN INSTRUMENT OF SERVICES, IS INTENDED ONLY FOR THE USE OF THE CONTRACTOR AND IS NOT TO BE COPIED OR REPRODUCED. USE OF AND IMPROPER RELIANCE ON THIS DOCUMENT WITHOUT THE WRITTEN APPROVAL AND ADAPTATION BY DPE ARCHITECTS PTE LTD SHALL BE WITHOUT LIABILITY TO DPE ARCHITECTS PTE LTD.			
DEVELOPER / LANDOWNER	PURAVANKARA LTD		
DESIGN EXECUTION	COWRKS		
PHE, FIRE, HVAC & ELECTRICAL CONSULTANTS			
KEY PLAN			
NORTH			
PROJECT TITLE	COWRKS PURVA PREMIERE RESIDENCY ROAD BENGALURU		
DRAWING TITLE	FURNITURE LAYOUT NINTH FLOOR.		
SCALE	DATE	DESIGNED	DRAWN
1:125	20.12.18	RATI	VB
STAGE	CONTRACT	CHECKED	APPROVED
-		PSN	TEJ
JOB NO.	DRAWING NO.	REV.	
	PP_CW_9F_901		RO
THIS DRAWING IS THE PROPERTY OF COWRKS NO PART OF THE DRAWING MAY BE REPRODUCED IN ANY MANNER WHATSOEVER WITHOUT PERMISSION FROM COWRKS			
GOOD FOR CONSTRUCTION			

